


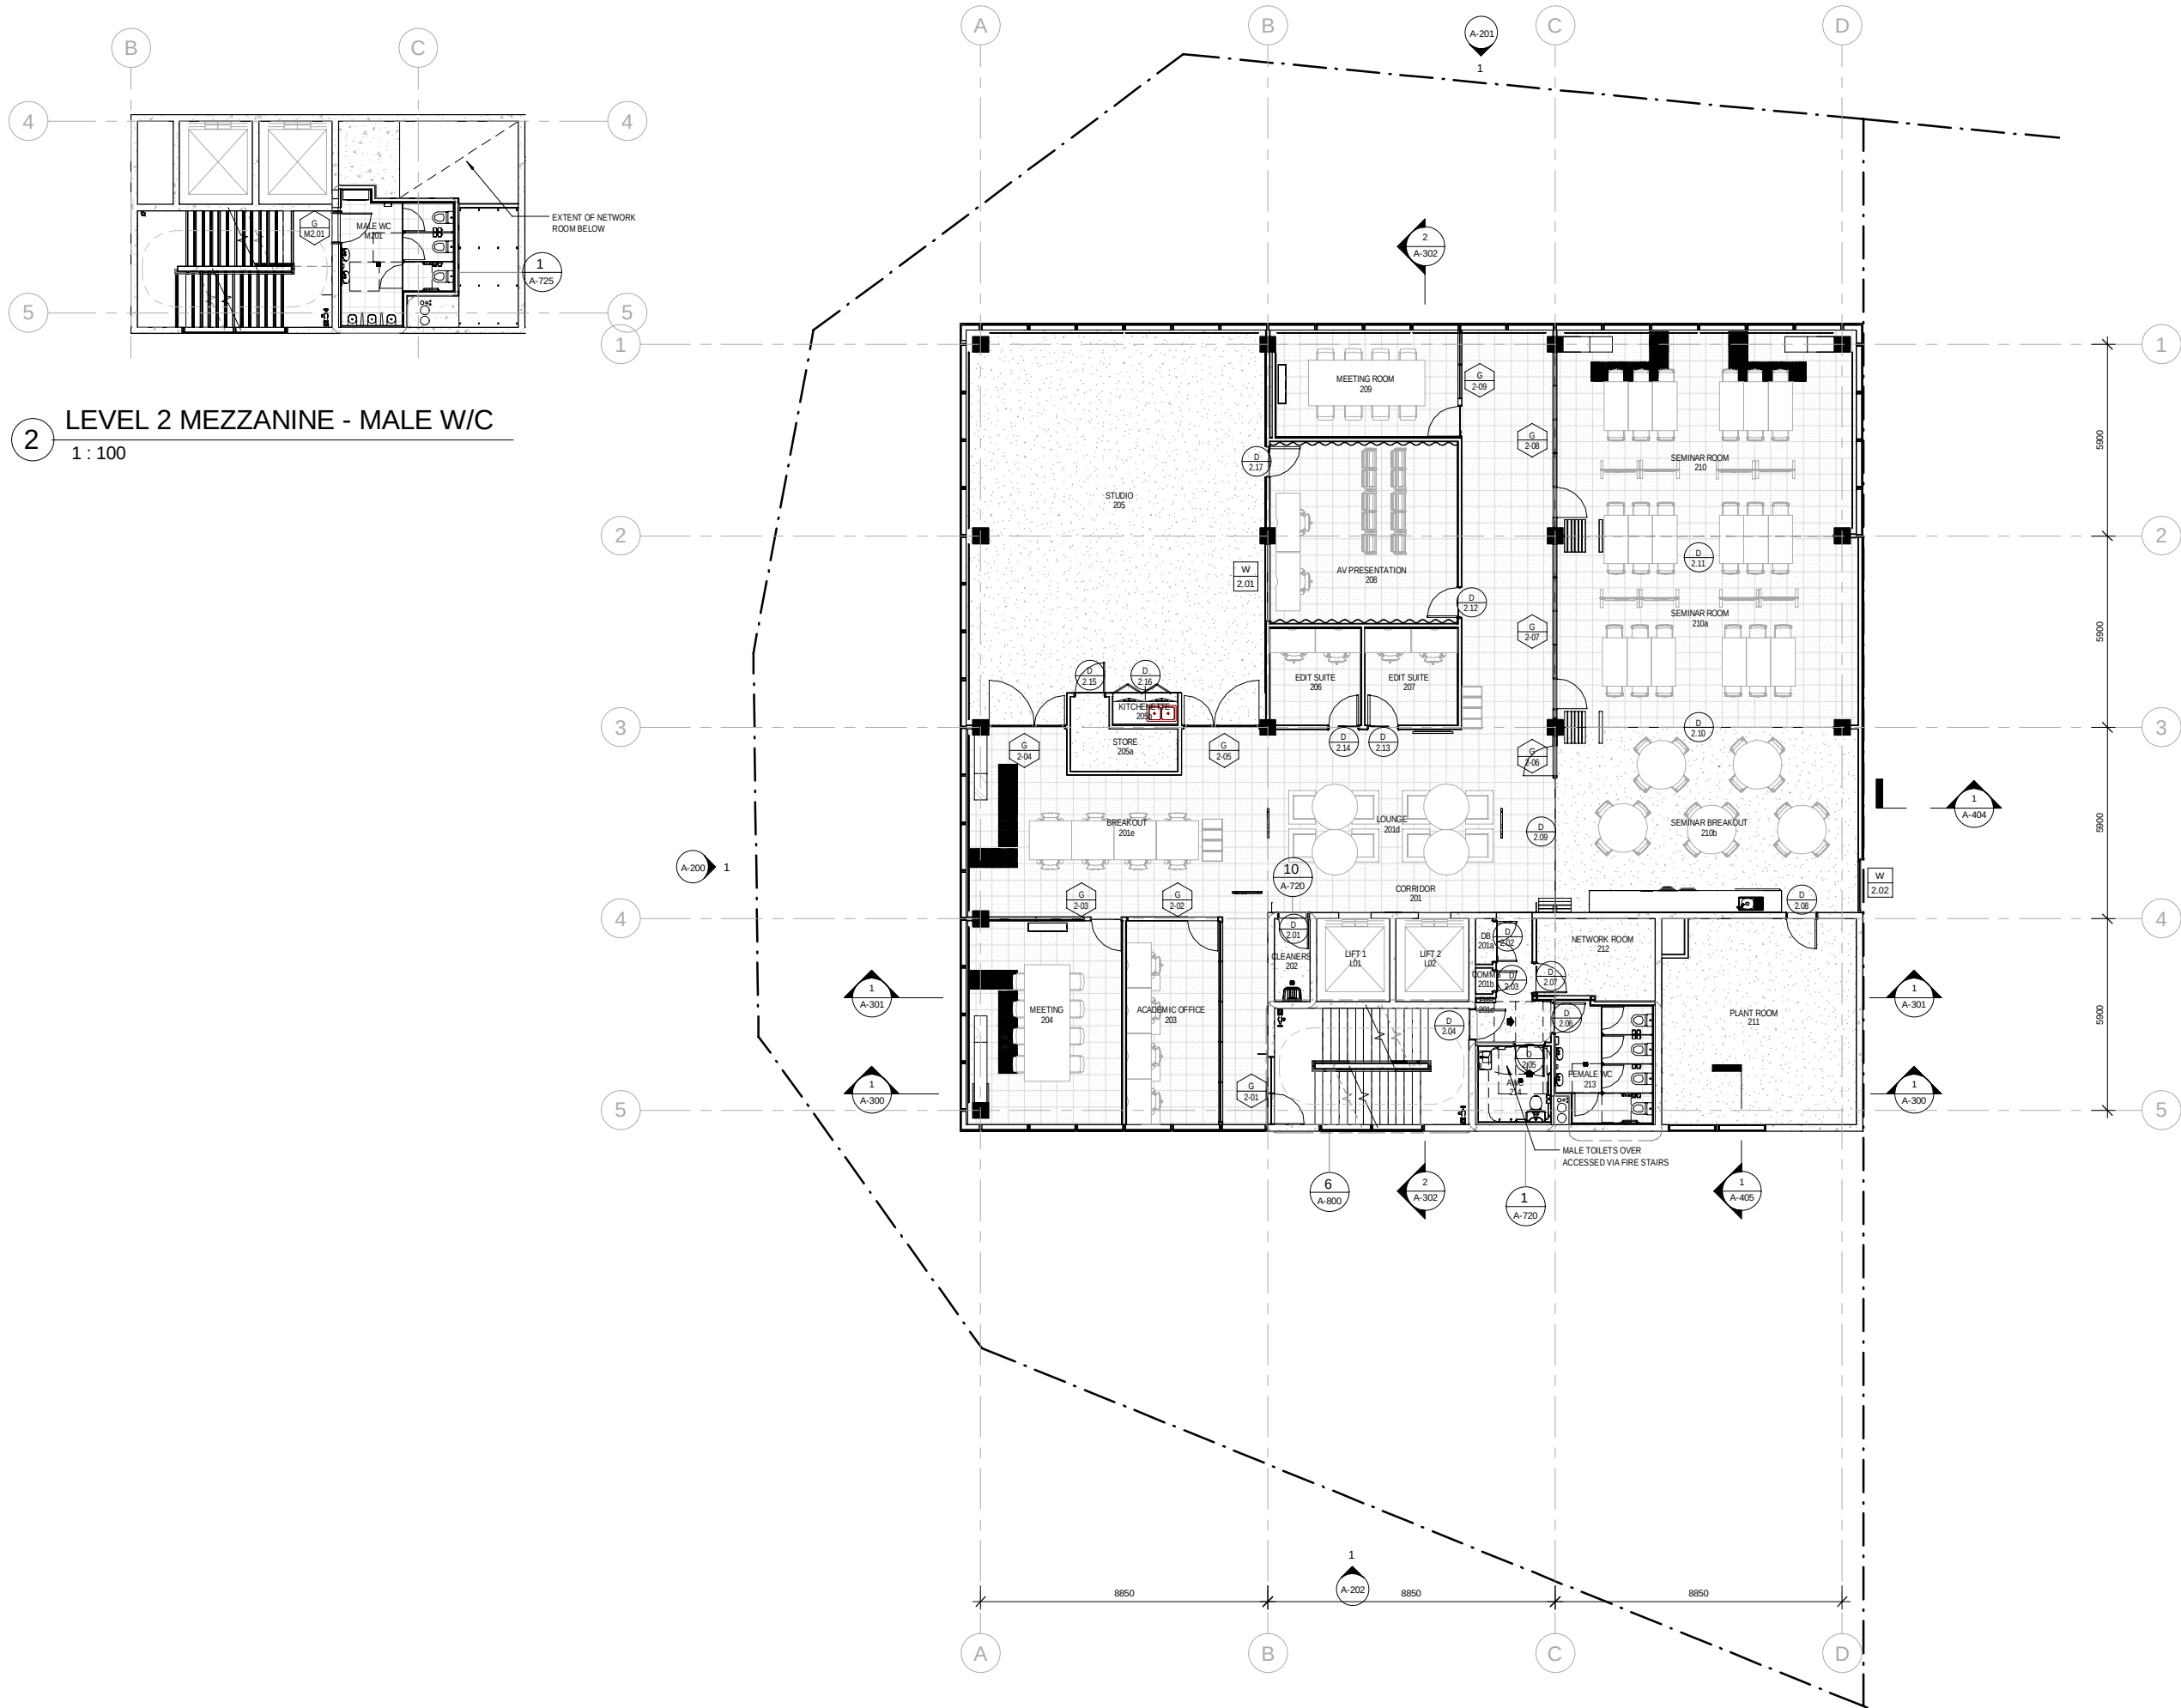

EJE ARCHITECTURE
ACN 002 912 843 | ABN 82 644 649 849
Nominated Architect - Bernard Collins
P +61 2 4929 2253 | F +61 2 4929 3069 | E mail@eye.com.au | W www.eye.com.au
A 412 KING STREET, NEWCASTLE, NSW 2300

COMPLETION OF THE QUALITY ASSURANCE CHECKS IS VERIFICATION THAT THE DOCUMENT CONFORMS WITH THE REQUIREMENTS OF THE QUALITY PROJECT PLAN. WHERE THE QUALITY ASSURANCE CHECK IS INCOMPLETE, THIS DOCUMENT IS PRELIMINARY FOR INFORMATION PURPOSES ONLY, OR SUCH PURPOSES AS STATED IN THE REVISION COLUMN.

THE IDEAS, INFORMATION AND CONCEPTS CONTAINED IN THIS DOCUMENT ARE THE PROPERTY OF EJE ARCHITECTURE. PHOTOCOPYING OR REPRODUCING THIS DOCUMENT AND PASSING IT ON TO OTHERS WITHOUT THE EXPRESS PERMISSION OF EJE ARCHITECTURE IS AN INFRINGEMENT OF COPYRIGHT.

0 25mm 100mm 200mm ON ORIGINAL A1



REV	DATE	COMMENTS
L	2019/01/18	ISSUE FOR SCHEMATIC DESIGN
M	2019/02/18	ISSUE FOR SSD
N	2019/05/08	DRAFT ISSUE FOR INFORMATION
P	2019/05/23	ISSUE FOR INFORMATION
Q	2019/05/28	ISSUE FOR INFORMATION
R	2019/06/21	ISSUE FOR INFORMATION
S	2019/06/26	ISSUE FOR TENDER REVIEW
T	2019/07/01	ISSUE FOR COORDINATION
U	2019/07/04	ISSUE FOR COORDINATION
V	2019/07/11	ISSUE FOR COORDINATION
1	2019/07/16	ISSUE FOR TENDER
	2019/16/12	ISSUE FOR SSD

DRN	CHKD	VRFD
JE	AKF	
JE	AKF	
JE	AKF	
JE	AKF	
JE	AKF	
JE	AKF	
JE	AKF	
JE	AKF	
NJH	JE	
NJH	JE	
JE	AKF	
JE	AKF	

PROJECT: HCCD STAGE 1A
CLIENT: UNIVERSITY OF NEWCASTLE

SITE: 16B HONEYSUCKLE DRIVE
NEWCASTLE, NSW, 2300
DRAWING: LEVEL 2 PLAN

WORK IN FIGURED DIMENSIONS IN PREFERENCE TO SCALE. CHECK DIMENSIONS AND LEVELS ON SITE PRIOR TO THE ORDERING OF MATERIALS OR THE COMPLETION OF WORKSHOP DRAWINGS. IF IN DOUBT ASK. REPORT ALL ERRORS AND OMISSIONS.

C:\Users\jevans\Documents\HCCD - STAGE 1A_Jevans@eye.com.au\rv

DRAWN: NJH
DATE: SEP 2018
SCALES: 1:100@A1
1:200@A3

PROJECT No: 11749
PHASE: TD
DRAWING No: A-102
REV: SSD

